
Kitchen equipment layout

For commercial kitchen equipment vendors · plan at 1:25 on A3 · every item named and sized on the drawing

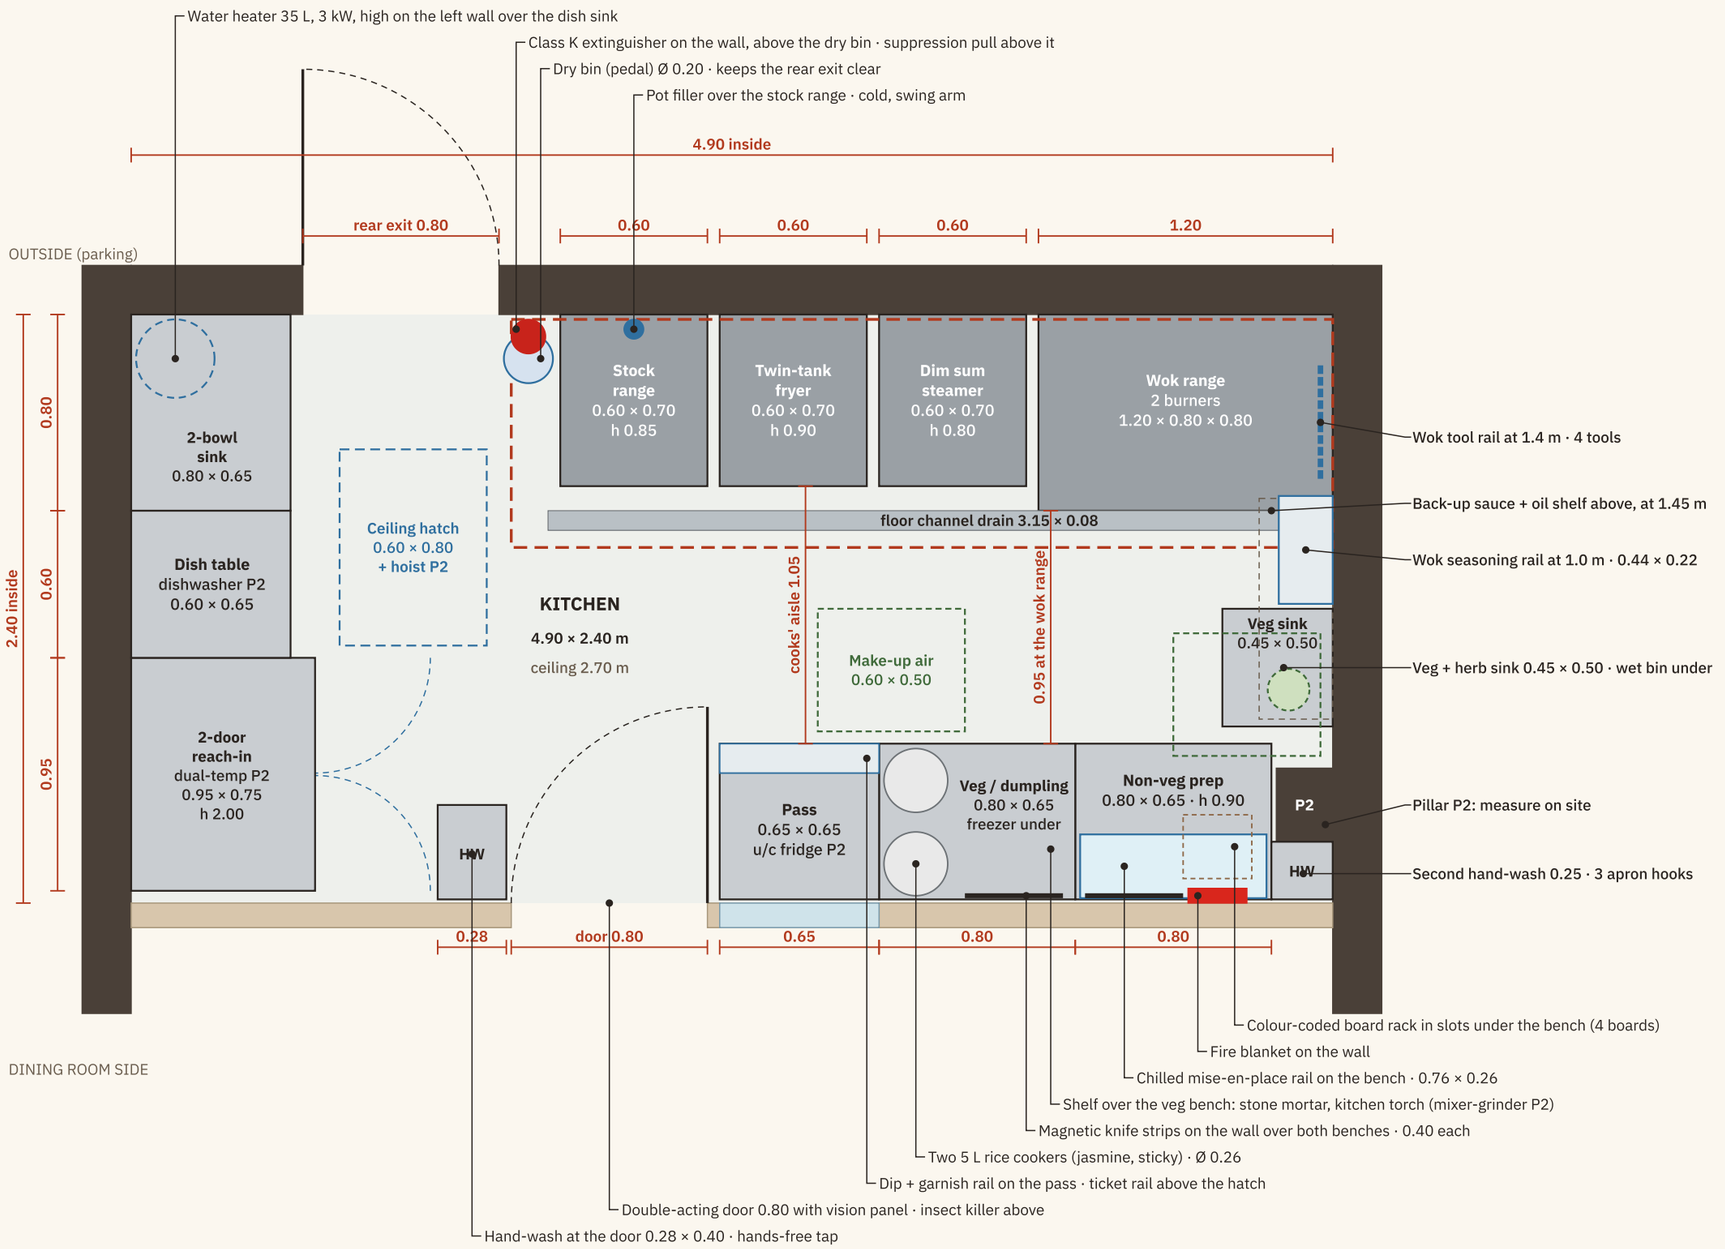

0 — 1 m — 2 m

PLAN 1:25 on A3 · dimensions in metres

Back wall at the top, dining room at the bottom; left and right as you walk in from the road. Dashed red: canopy hood above (3.35 × 0.95, bottom 2.05 m).

Dashed blue: hatch and fridge doors. Dashed green: make-up air diffusers above (2). Dashed grey: shelves above. Heights and services: sheet 2.

Equipment list

EQUIPMENT	W × D × H (m)	QTY
Wok range, 2 burners (Chinese)	1.20 × 0.80 × 0.80	1
Dim sum steamer, 2 holes	0.60 × 0.70 × 0.80	1
Twin-tank fryer (veg / non-veg)	0.60 × 0.70 × 0.90	1
Stock range, 2 burners	0.60 × 0.70 × 0.85	1
Canopy hood, baffle filters, suppression	3.35 × 0.95 × 0.55	1
Non-veg prep bench, undershelf, shelf over	0.80 × 0.65 × 0.90	1
Veg / dumpling bench, 2 shelves over	0.80 × 0.65 × 0.90	1
Under-counter freezer (in the veg bench)	2 doors	1
Pass bench + 2 heat lamps	0.65 × 0.65 × 0.90	1
Pass under-counter fridge	0.60 × 0.55 × 0.70	1 · P2
Veg + herb wash sink, tall mixer tap	0.45 × 0.50 × 0.90	1
Hand-wash basins, hands-free, 6 L heater each	0.28 × 0.40 · 0.25 × 0.25	2
Reach-in, 2-door (dual-temp upgrade P2)	0.95 × 0.75 × 2.00	1
Dish table (under-counter dishwasher P2)	0.60 × 0.65 × 0.90	1
2-bowl sink + pre-rinse spray	0.80 × 0.65 × 0.90	1
Storage water heater 35 L, 3 kW	Ø 0.33 × 0.50	1
Shelves over the dish line (top one slatted)	1.40 × 0.35	2
Bamboo steamer stacks (3 baskets + lid)	Ø 0.26	3
Pot filler, wall swing arm (cold)	0.30 reach	1
Used-oil can 20 L + spill tray	0.34 × 0.17 × 0.40	1
Wok seasoning rail, 8 pots + 8 bottles	0.44 × 0.22	1
Wok tool rail: ladle, spatula, spider, brush	0.47	1
Back-up sauce + oil shelf	0.90 × 0.30	1
Chilled mise-en-place rail, 5 pans	0.76 × 0.26 × 0.22	1
Dip + garnish rail (5 inserts)	0.65 × 0.12	1
Ticket rail over the pass hatch	0.65	1
Magnetic knife strips	0.40	2
Colour-coded board rack + boards	4 boards	1
Rice cookers 5 L (jasmine, sticky)	Ø 0.26	2
Stone mortar + pestle, granite	Ø 0.22	1
Mixer-grinder, commercial	—	1 · P2
Kitchen blowtorch	—	1
Foot-pedal bins (wet under veg sink, dry)	Ø 0.20 × 0.60	2
Apron hook rail at the prep corner	3 hooks	1
Double-acting door, vision panel, kick plate	0.80 × 2.05	1
Make-up air diffusers, ceiling	0.60 × 0.50	2
Insect killer	0.50 × 0.18	1
Floor channel drain	3.15 × 0.08	1
Ceiling hatch + fold-down ladder	0.60 × 0.80	1
Goods hoist 200 kg over the hatch	—	1 · P2
Extinguisher Class K 6 L (CO_2 at the door)	wall bracket	1
Fire blanket, first-aid box	—	1 each
OUTSIDE + SERVICES (details on sheet 2)		
LPG bank: cage + 4 × 19 kg (5th spare P2)	0.35 × 1.70 × 1.60	1
Gas: solenoid valve, valve per appliance, leak detector	copper, 1 set	1
Exhaust: ESP + carbon filter, outside	0.50 × 1.00 × 0.90	1
Inline exhaust fan, anti-vibration mounts	Ø 0.44	1
Fresh-air intake fan, back wall, high	0.50 × 0.48	1
Cooling coil 1.5 TR + condenser (make-up air)	0.80 × 0.55 × 0.30	1 · P2
Grease trap, outside back corner	0.45 × 0.45	1
Water cabinet: pump, filter, softener	0.45 × 0.80 × 1.50	1 · P2
Water sump, buried, 1,000 L	1.3 × 1.0 × 0.8	1 · P2
Heat detector, kitchen ceiling	—	1
Sockets 1–14, fan + ESP control panel	sheet 2	1 set

NOTES

Stainless steel 304 benches, 0.90 m high; hot line 0.70 deep, wok range 0.80. Cooks' aisle 1.05 m (0.95 m at the wok range). Cement-board ceiling at 2.70 m; storage deck above, hoist at the hatch. Pan-Asian menu: about 23 recipes, 40 choices; one chef + one helper. P2 = phase 2: bought after opening; space and services reserved now. Positions are from the 3D model: check walls and pillar P2 on site.