
Kitchen equipment layout

For commercial kitchen equipment vendors · plan at 1:25 on A3 · every item named and sized on the drawing

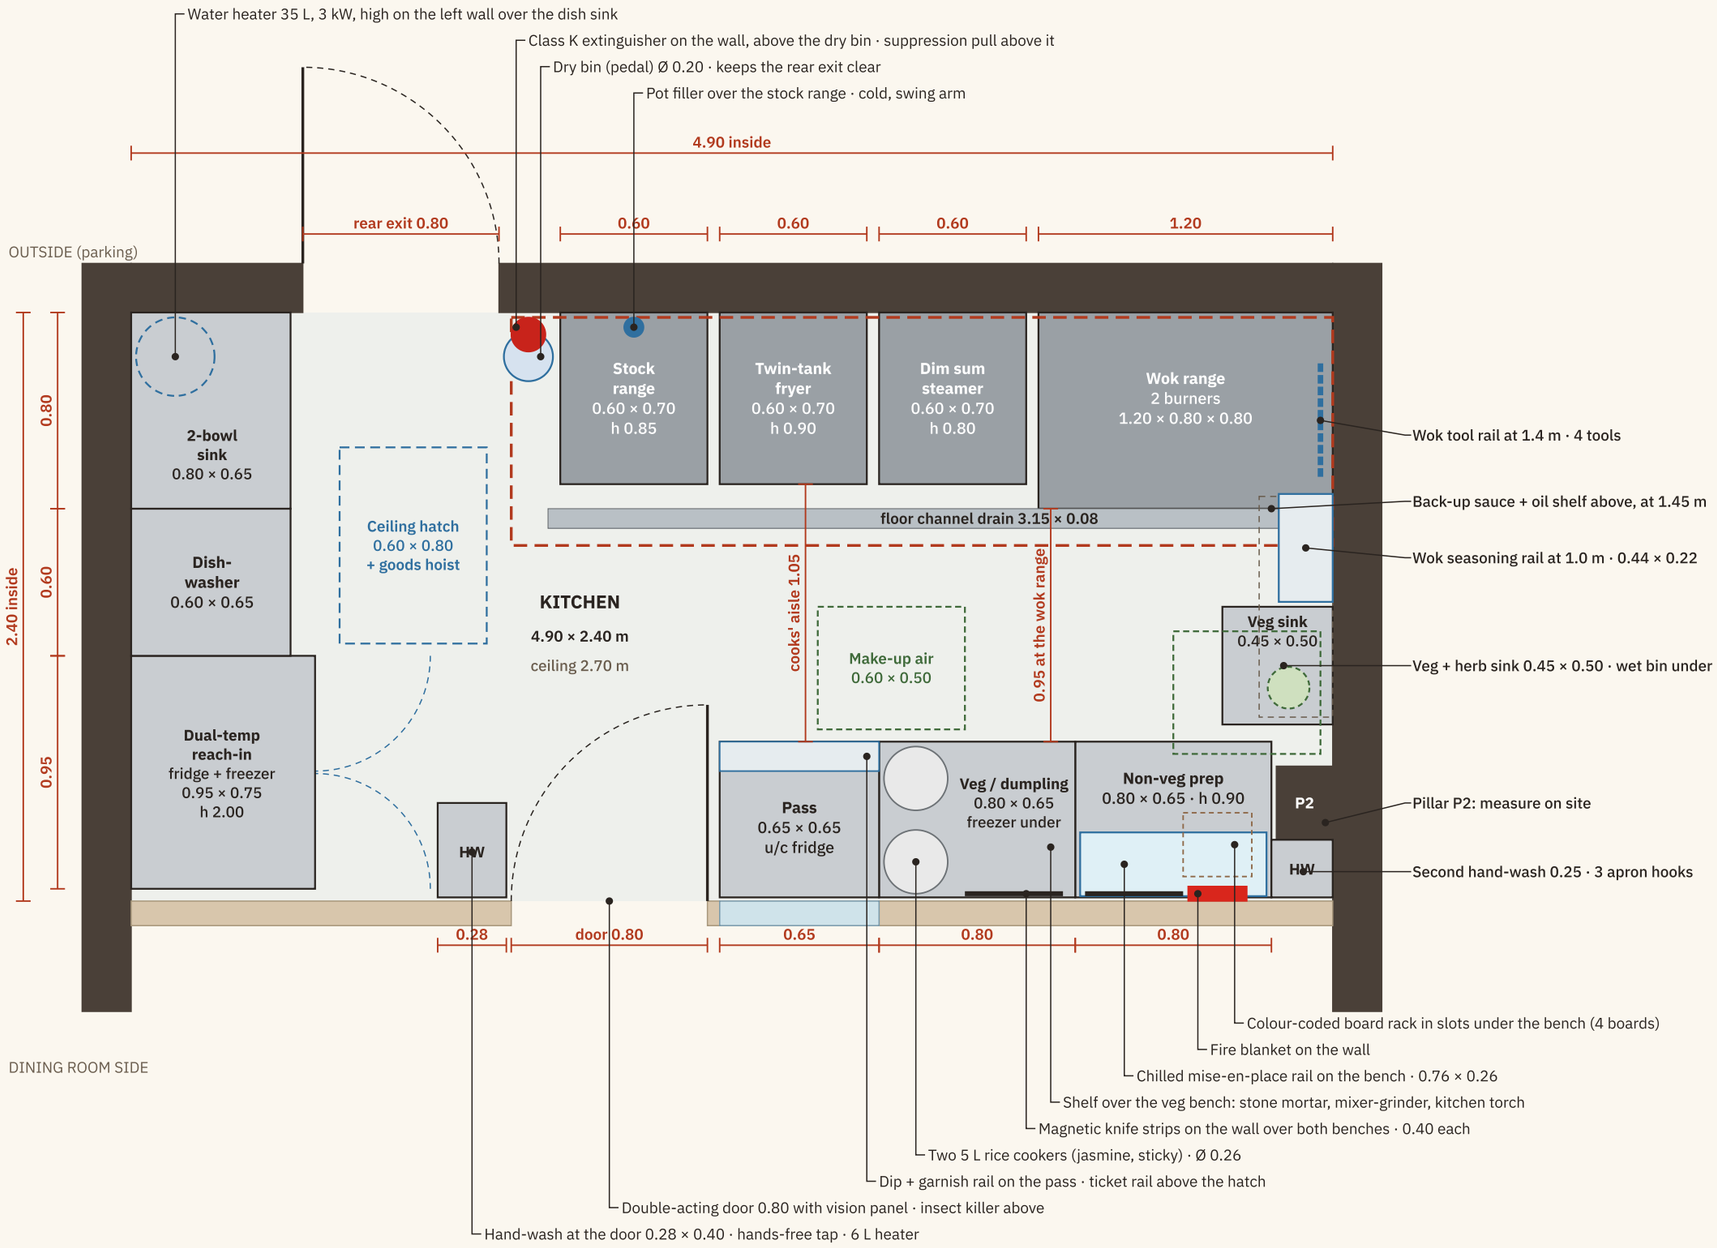

Equipment list = BOQ sections A and B

NO	EQUIPMENT / TYPE	SIZE W × D × H (mm)	QTY
A	STAINLESS STEEL FABRICATION (SS 304 THROUGHOUT)		
A.01	Non-veg prep bench	800 × 650 × 900	1 nos
A.02	Dumpling and veg prep bench	800 × 650 × 900	1 nos
A.03	Pass counter	650 × 650 × 900	1 nos
A.04	Dish sink, 2 bowls	800 × 650 × 900	1 nos
A.05	Wall shelf over the dish line	1,400 × 350	2 nos
A.06	Veg and herb wash sink	450 × 500 × 900	1 nos
A.07	Sauce and oil wall shelf	900 × 300	1 nos
A.08	Wok seasoning rail	440 × 220	1 set
A.09	Wok tool rail	470 long	1 nos
A.10	Chilled mise-en-place rail	760 × 260 × 220	1 nos
A.11	Dip and garnish rail	650 × 120	1 nos
A.12	Ticket rail	650 long	1 nos
A.13	Magnetic knife strip	400 long	2 nos
A.14	Cutting-board rack	280 × 420 × 420	1 nos
A.15	Floor channel drain	3,150 × 80	3.15 m
A.16	Canopy hood	3,350 × 950 × 550	1 nos
A.17	Exhaust ductwork	400 × 400	5 m
A.18	Discharge elbow	400 × 400	1 nos
A.19	Storage deck racking	3 sizes, see BOQ	3 nos
A.20	Ceiling hatch frame with fold-down ladder	600 × 800 opening	1 nos
B	COOKING, COLD AND KITCHEN EQUIPMENT (BRANDED)		
B.01	Chinese wok range, 2 burners	1,200 × 800 × 800	1 nos
B.02	Dim sum steamer, 2 holes	600 × 700 × 800	1 nos
B.03	Twin-tank fryer	600 × 700 × 900	1 nos
B.04	Stock range, 2 burners	600 × 700 × 850	1 nos
B.05	Reach-in, 2 doors, dual temperature	950 × 750 × 2,000	1 nos
B.06	Under-counter fridge (pass)	600 × 550 × 700	1 nos
B.07	Under-counter freezer, 2 doors	fits under 800 × 650	1 nos
B.08	Under-counter dishwasher	600 × 650 × 900	1 nos
B.09	Rice cooker	Ø 260	2 nos
B.10	Mixer-grinder		1 nos
B.11	Kitchen blowtorch		1 nos
B.12	Storage water heater	Ø 330 × 500	1 nos
B.13	Water heater for a hand-wash basin		2 nos
B.14	Insect killer	500 × 180	1 nos
B.15	Heat lamp over the pass		2 nos
B.16	ESP with carbon odour filter	500 × 1,000 × 900	1 nos
B.17	Inline exhaust fan	Ø 440	1 nos
B.18	Fresh-air intake fan	500 × 480	1 nos
B.19	Make-up air diffuser	600 × 500	2 nos
B.20	Make-up air cooling coil with condenser	condenser 800 × 550 × 300	1 set
B.21	Goods hoist		1 nos
B.22	Smallware		1 lot
B.23	Bamboo steamer stack	Ø 260	3 nos
C–H	Gas, plumbing, electrical, civil, fire, outside: see the BOQ		

NOTES

Stainless steel 304 benches, 0.90 m high; hot line 0.70 deep,
wok range 0.80. Cooks' aisle 1.05 m (0.95 m at the wok range).
Cement-board ceiling at 2.70 m; storage deck above, hoist at the hatch.
Pan-Asian menu: about 23 recipes, 40 choices; one chef + one helper.
Price against the BOQ (boq.html): item numbers, units, quantities.
Positions are from the 3D model: check walls and pillar P2 on site.

0 — 1 m — 2 m

PLAN 1:25 on A3 · dimensions in metres

Back wall at the top, dining room at the bottom; left and right as you walk in from the road. Dashed red: canopy hood above (3.35 × 0.95, bottom 2.05 m).
Dashed blue: hatch and fridge doors. Dashed green: make-up air diffusers above (2). Dashed grey: shelves above. Heights and services: sheet 2.