
Kitchen equipment layout

For commercial kitchen equipment vendors · plan at 1:25 on A3 · every item named and sized on the drawing

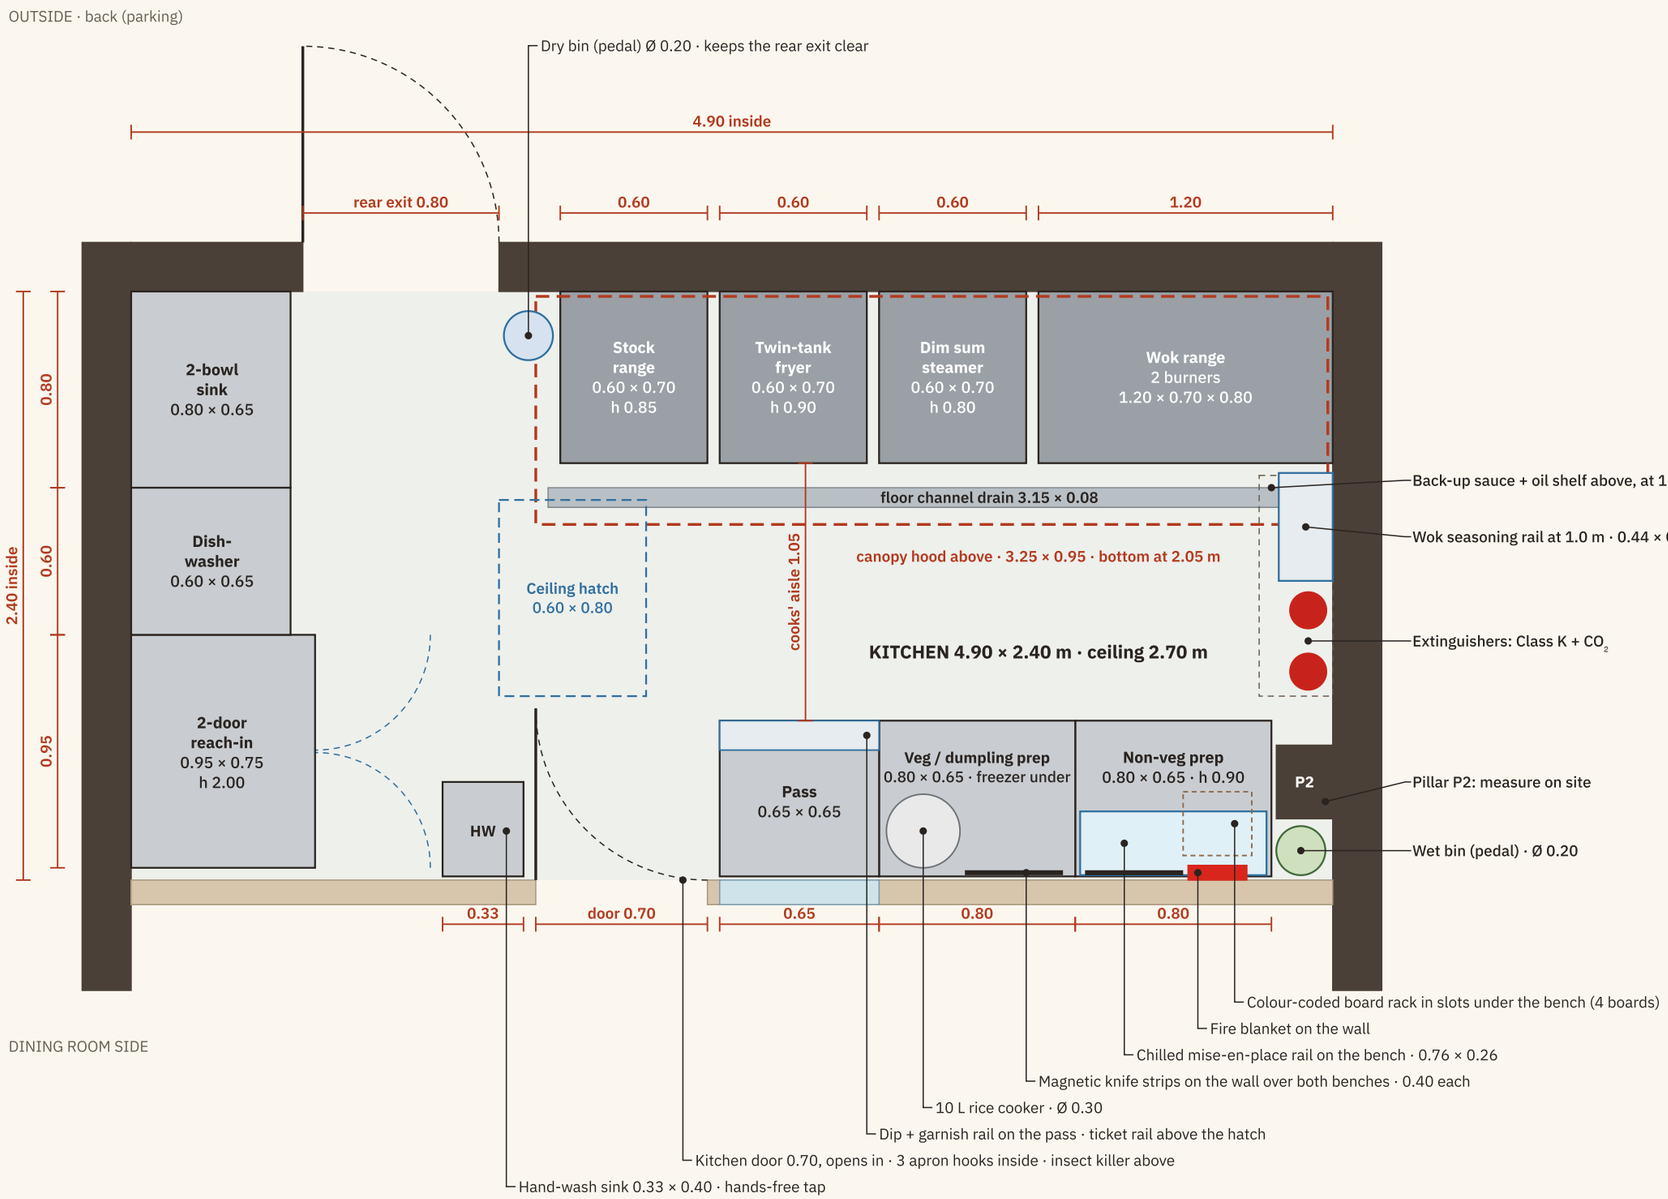

0 — 1 m — 2 m

PLAN 1:25 on A3 · dimensions in metres

Back wall at the top, dining room at the bottom; left and right as you walk in from the road. Dashed red: canopy hood above.
Dashed blue: ceiling hatch and fridge door swings. Dashed grey: shelves above. Heights, exhaust and services: sheet 2.

Equipment list

EQUIPMENT	W × D × H (m)	QTY
Wok range, 2 burners (Chinese)	1.20 × 0.70 × 0.80	1
Dim sum steamer, 2 holes	0.60 × 0.70 × 0.80	1
Twin-tank fryer (veg / non-veg)	0.60 × 0.70 × 0.90	1
Stock range, 2 burners	0.60 × 0.70 × 0.85	1
Canopy hood, baffle filters, suppression	3.25 × 0.95 × 0.55	1
Non-veg prep bench, undershelf, shelf over	0.80 × 0.65 × 0.90	1
Veg / dumpling bench, 2 shelves over	0.80 × 0.65 × 0.90	1
Under-counter freezer (in the veg bench)	2 doors	1
Pass bench + 2 heat lamps	0.65 × 0.65 × 0.90	1
Hand-wash sink, hands-free tap	0.33 × 0.40	1
2-door reach-in fridge	0.95 × 0.75 × 2.00	1
Under-counter dishwasher + drainboard	0.60 × 0.65 × 0.90	1
2-bowl sink + pre-rinse spray	0.80 × 0.65 × 0.90	1
Shelves over the dish line	1.40 × 0.35	2
Wok seasoning rail, 8 pots + 8 bottles	0.44 × 0.22	1
Back-up sauce + oil shelf	0.90 × 0.30	1
Chilled mise-en-place rail, 5 pans	0.76 × 0.26 × 0.22	1
Dip + garnish rail (5 inserts)	0.65 × 0.12	1
Ticket rail over the pass hatch	0.65	1
Magnetic knife strips	0.40	2
Colour-coded board rack + boards	4 boards	1
10 L rice cooker	Ø 0.30	1
Foot-pedal bins (wet, dry)	Ø 0.20 × 0.60	2
Apron hook rail on the door	3 hooks	1
Insect killer	0.50 × 0.18	1
Floor channel drain	3.15 × 0.08	1
Ceiling hatch + fold-down ladder	0.60 × 0.80	1
Extinguishers: Class K 6 L, CO_2 4.5 kg	wall brackets	2
Fire blanket, first-aid box	—	1 each

NOTES

Benches stainless steel 304, 0.90 m high; hot line 0.70 deep.
Kitchen 4.90 × 2.40 m inside; PVC ceiling at 2.70 m with a storage deck above (1.7 m clear) reached by the hatch.
Sized to the 22-dish menu: Tangra Indo-Chinese wok dishes, dim sum, bao, Korean bar food; about 60–80 covers a day.
Positions are from the 3D model; check every wall and pillar P2 on site before fabrication.