
Kitchen equipment layout

For commercial kitchen equipment vendors · plan at 1:25 on A3 · every item named and sized on the drawing

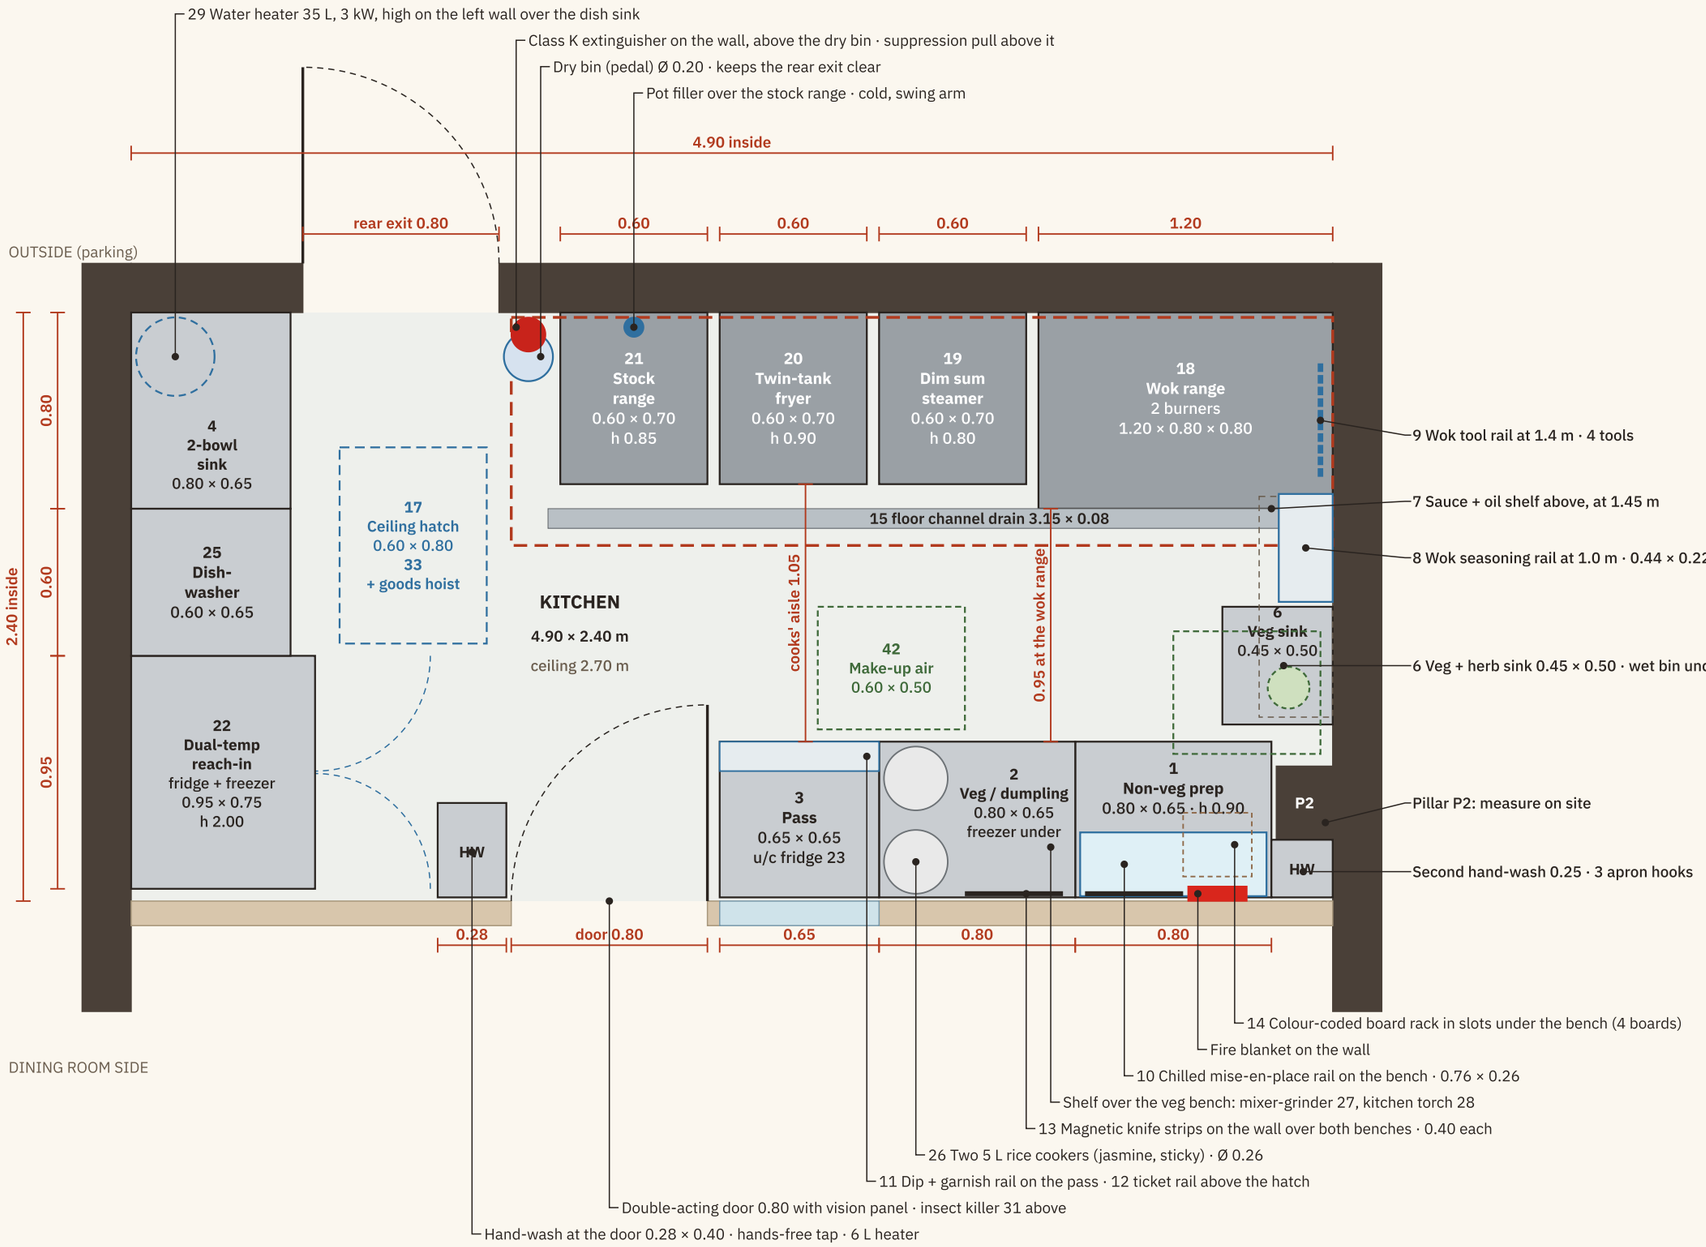

0 — 1 m — 2 m

PLAN 1:25 on A3 · dimensions in metres

Back wall at the top, dining room at the bottom; left and right as you walk in from the road. Dashed red: canopy hood above (3.35 × 0.95, bottom 2.05 m).
Dashed blue: hatch and fridge doors. Dashed green: make-up air diffusers above (2). Dashed grey: shelves above. Heights and services: sheet 2.

Equipment list: the same numbers 1 to 44 as the BOQ


NO	EQUIPMENT / TYPE	SIZE W × D × H (mm)	QTY
	STAINLESS STEEL FABRICATION		
1	Non-veg prep bench	800 × 650 × 900	1 nos
2	Dumpling and veg prep bench	800 × 650 × 900	1 nos
3	Pass counter	650 × 650 × 900	1 nos
4	Dish sink, 2 bowls	800 × 650 × 900	1 nos
5	Wall shelf over the dish line	1,400 × 350	2 nos
6	Veg and herb wash sink	450 × 500 × 900	1 nos
7	Sauce and oil wall shelf	900 × 300	1 nos
8	Wok seasoning rail	440 × 220	1 set
9	Wok tool rail	470 long	1 nos
10	Chilled mise-en-place rail	760 × 260 × 220	1 nos
11	Dip and garnish rail	650 × 120	1 nos
12	Ticket rail	650 long	1 nos
13	Magnetic knife strip	400 long	2 nos
14	Cutting-board rack	280 × 420 × 420	1 nos
15	Floor channel drain	3,150 × 80	3.15 m
16	Storage deck racking	3 sizes, see BOQ	3 nos
17	Ceiling hatch frame with fold-down ladder	600 × 800 opening	1 nos
	COOKING, COLD AND KITCHEN EQUIPMENT (BRANDED)		
18	Chinese wok range, 2 burners	1,200 × 800 × 800	1 nos
19	Dim sum steamer, 2 holes	600 × 700 × 800	1 nos
20	Twin-tank fryer	600 × 700 × 900	1 nos
21	Stock range, 2 burners	600 × 700 × 850	1 nos
22	Reach-in, 2 doors, dual temperature	950 × 750 × 2,000	1 nos
23	Under-counter fridge (pass)	600 × 550 × 700	1 nos
24	Under-counter freezer, 2 doors	fits under 800 × 650	1 nos
25	Under-counter dishwasher	600 × 650 × 900	1 nos
26	Rice cooker	Ø 260	2 nos
27	Mixer-grinder		1 nos
28	Kitchen blowtorch		1 nos
29	Storage water heater	Ø 330 × 500	1 nos
30	Water heater for a hand-wash basin		2 nos
31	Insect killer	500 × 180	1 nos
32	Heat lamp over the pass		2 nos
33	Goods hoist		1 nos
34	Smallware		1 lot
35	Bamboo steamer stack	Ø 260	3 nos
	HOOD, EXHAUST AND VENTILATION		
36	Canopy hood, wall type, with baffle filters	3,350 × 950 × 550	1 nos
37	Exhaust ducting, rectangular	400 × 400	5 m
38	Discharge elbow	400 × 400	1 nos
39	ESP with carbon odour filter	500 × 1,000 × 900	1 nos
40	Inline exhaust fan	Ø 440	1 nos
41	Fresh-air intake fan	500 × 480	1 nos
42	Make-up air diffuser, perforated, low velocity	600 × 500	2 nos
43	Make-up air cooling coil with condenser	condenser 800 × 550 × 300	1 set
44	Exhaust fan and ESP control panel		1 nos
	Gas, plumbing, electrical, civil, fire: main BOQ		

NOTES

Stainless steel 304 benches, 0.90 m high; hot line 0.70 deep,
wok range 0.80. Cooks' aisle 1.05 m (0.95 m at the wok range).
Cement-board ceiling at 2.70 m; storage deck above, hoist at the hatch.
Pan-Asian menu: about 23 recipes, 40 choices; one chef + one helper.
The numbers 1 to 44 on the items are the BOQ numbers (boq.html).
Positions are from the 3D model: check walls and pillar P2 on site.

Kitchen services and exhaust

For kitchen equipment, exhaust, gas, plumbing and electrical vendors · plan at 1:25 and elevation at 1:40 on A3

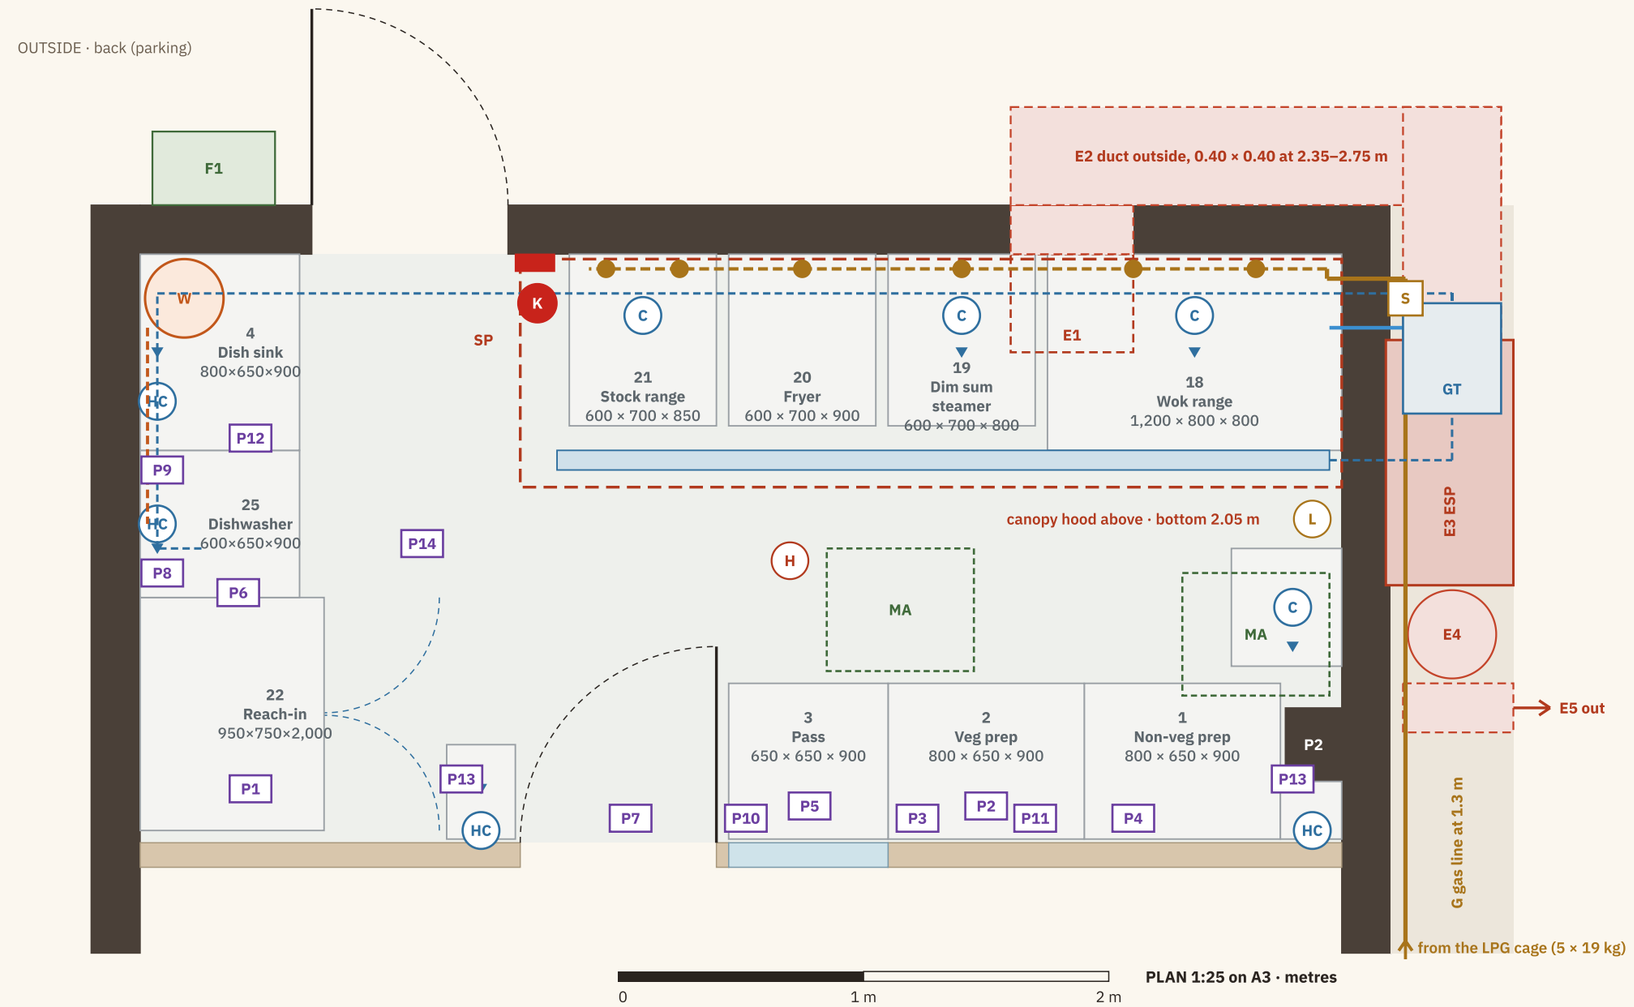

Services list

TAG	ITEM	SIZE / NOTE
E1	Duct through the back wall	0.40 × 0.40 at 2.35–2.75 m
E2	Duct along the wall, round the corner	0.40 × 0.40, outside
E3	ESP + carbon odour filter	0.50 × 1.00 × 0.90, 2.05–2.95 m
E4	Inline exhaust fan	Ø 0.44 · on backup
E5	Side discharge, mesh + rain cowl	0.40 × 0.40 at ~2.6 m
F1	Fresh-air intake fan, back wall	0.50 × 0.48 at 3.3 m
MA	Make-up air diffusers ×2, ceiling	0.60 × 0.50 each · ~2.4 m/s
CC	Cooling coil in the make-up duct	1.5 TR · 3rd condenser on the wall
G	LPG line, copper, from the cage	at 1.3 m, in at the back corner
S	Solenoid valve on the entry, outside	interlocked: fan + suppression
SP	Hood suppression pull + gas cut-off	at the rear exit, 1.3–1.5 m
GT	Grease trap, outside back corner	0.45 × 0.45
W	Storage water heater, 3 kW	35 L · left wall over the sink
PF	Pot filler, cold, swing arm	over the stock range
WC	Water cabinet: pump, filter, softener	outside, 1.2–2.0 m · on backup
SU	Water sump, buried	1,000 L · 1.3 × 1.0 × 0.8 · garden
P1	Reach-in fridge	1-ph socket · on backup
P2	Under-counter freezer	1-ph socket · on backup
P3	Two rice cookers	twin 1-ph socket
P4	Chilled mise-en-place rail	1-ph socket · on backup
P5	Heat lamps over the pass	1-ph, switched
P6	Dishwasher	1-ph or 3-ph: confirm model
P7	Insect killer	1-ph
P8	Hood-light switch	left wall, by panel P9
P9	Exhaust fan + ESP control panel	left wall over the DW · on backup
P10	Pass under-counter fridge	1-ph socket · on backup
P11	Mixer-grinder	1-ph socket, 16 A
P12	Water heater isolator	own 3 kW MCB
P13	Hand-wash heaters ×2	1 kW each, 6 L
P14	Goods hoist over the hatch	200 kg · 0.4 kW

EXHAUST + AIR

Allow about 4,000–5,000 m³/h for the whole hood (vendor to size); about 8 m/s in the 0.40 × 0.40 duct. ESP + carbon filter before the fan. No roof stack: apartment above, parking behind. Hood overhang 0.20 m at the open end, 0.15 m over the wok range. Make-up air about 80% of the exhaust through two low-velocity diffusers (~2.4 m/s), cooled by a 1.5 TR coil, interlocked.

GAS

5 × 19 kg LPG (4 on the manifold + 1 full spare = 95 kg) in a locked cage on the right strip. Typical load: wok 2 × 18, stock 2 × 8, fryer 18, steamer 11 kW = about 80 kW connected, 55 kW at once; 4 cylinders give about 60–75 kW in Goa: vendor to confirm the burner ratings, add a vaporiser if they are higher. A valve per appliance; solenoid shuts off with the fan or the suppression; leak detector low on the right wall.


WATER + DRAINS

Cold: 1,000 L buried sump → pump, filter, softener cabinet (on backup) → kitchen. Hot: 35 L heater for the sink and pre-rinse, 6 L heaters under both hand-wash basins, dishwasher with its own booster. All kitchen drains to the grease trap, then the grey-water line (never the biodigester).

POWER

Shop supply: three-phase, about 15–20 kW. Backup 7.5 kVA covers the fridges, rails, fan, ESP, lights and the water pump. Not the ACs.

Hot line elevation · back wall seen from inside · 1:40 on A3

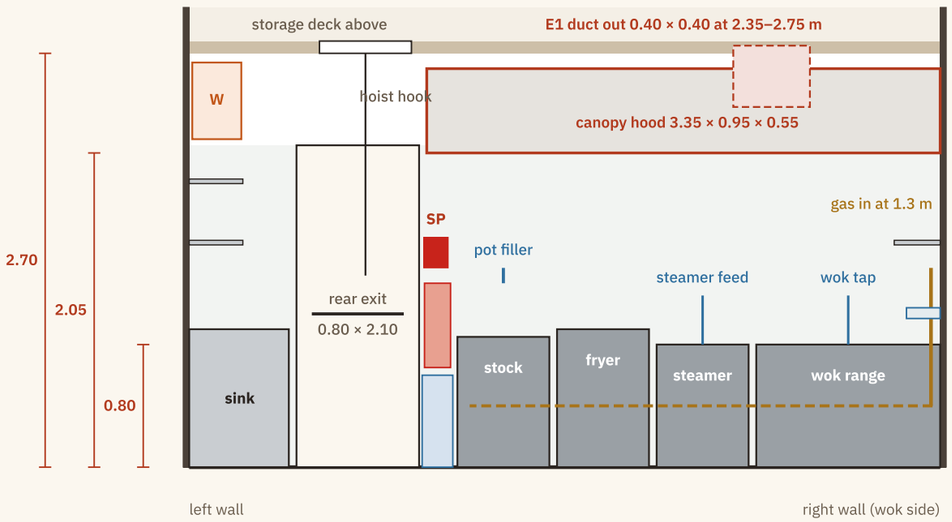

Legend: every symbol and letter on this sheet

- canopy hood outline (above)
- exhaust duct, outside, 2.35–2.75 m
- gas line, copper
- gas manifold at 0.40 m (dot = valve)
- S solenoid shut-off valve
- L gas leak detector
- HC water point, hot + cold
- C water point, cold only
- drain point
- drain line to the grease trap
- hot water pipe from heater W
- cold water main in (WM)
- GT grease trap (outside, back corner)
- W 35 L storage water heater
- P1 P1 to P14 power point (services list); plain numbers 1 to 44 are BOQ items
- MA make-up air diffusers, ceiling
- H heat detector
- K Class K extinguisher (wok and fryer fires)
- SP hood suppression pull + gas cut-off
- P1, P2 structural pillars on the right wall
- E, F, CC, G, WC, SU, PF: services list