
Ground floor plan · 4.9 × 8.8 m

Betalbatim pub · Concept 27 (mirrored: washroom right, bar left; 0.45 m min between tables) · from the shop drawing (47 m² super built-up) · 18 covers inside + 8 in the garden · 26 in all

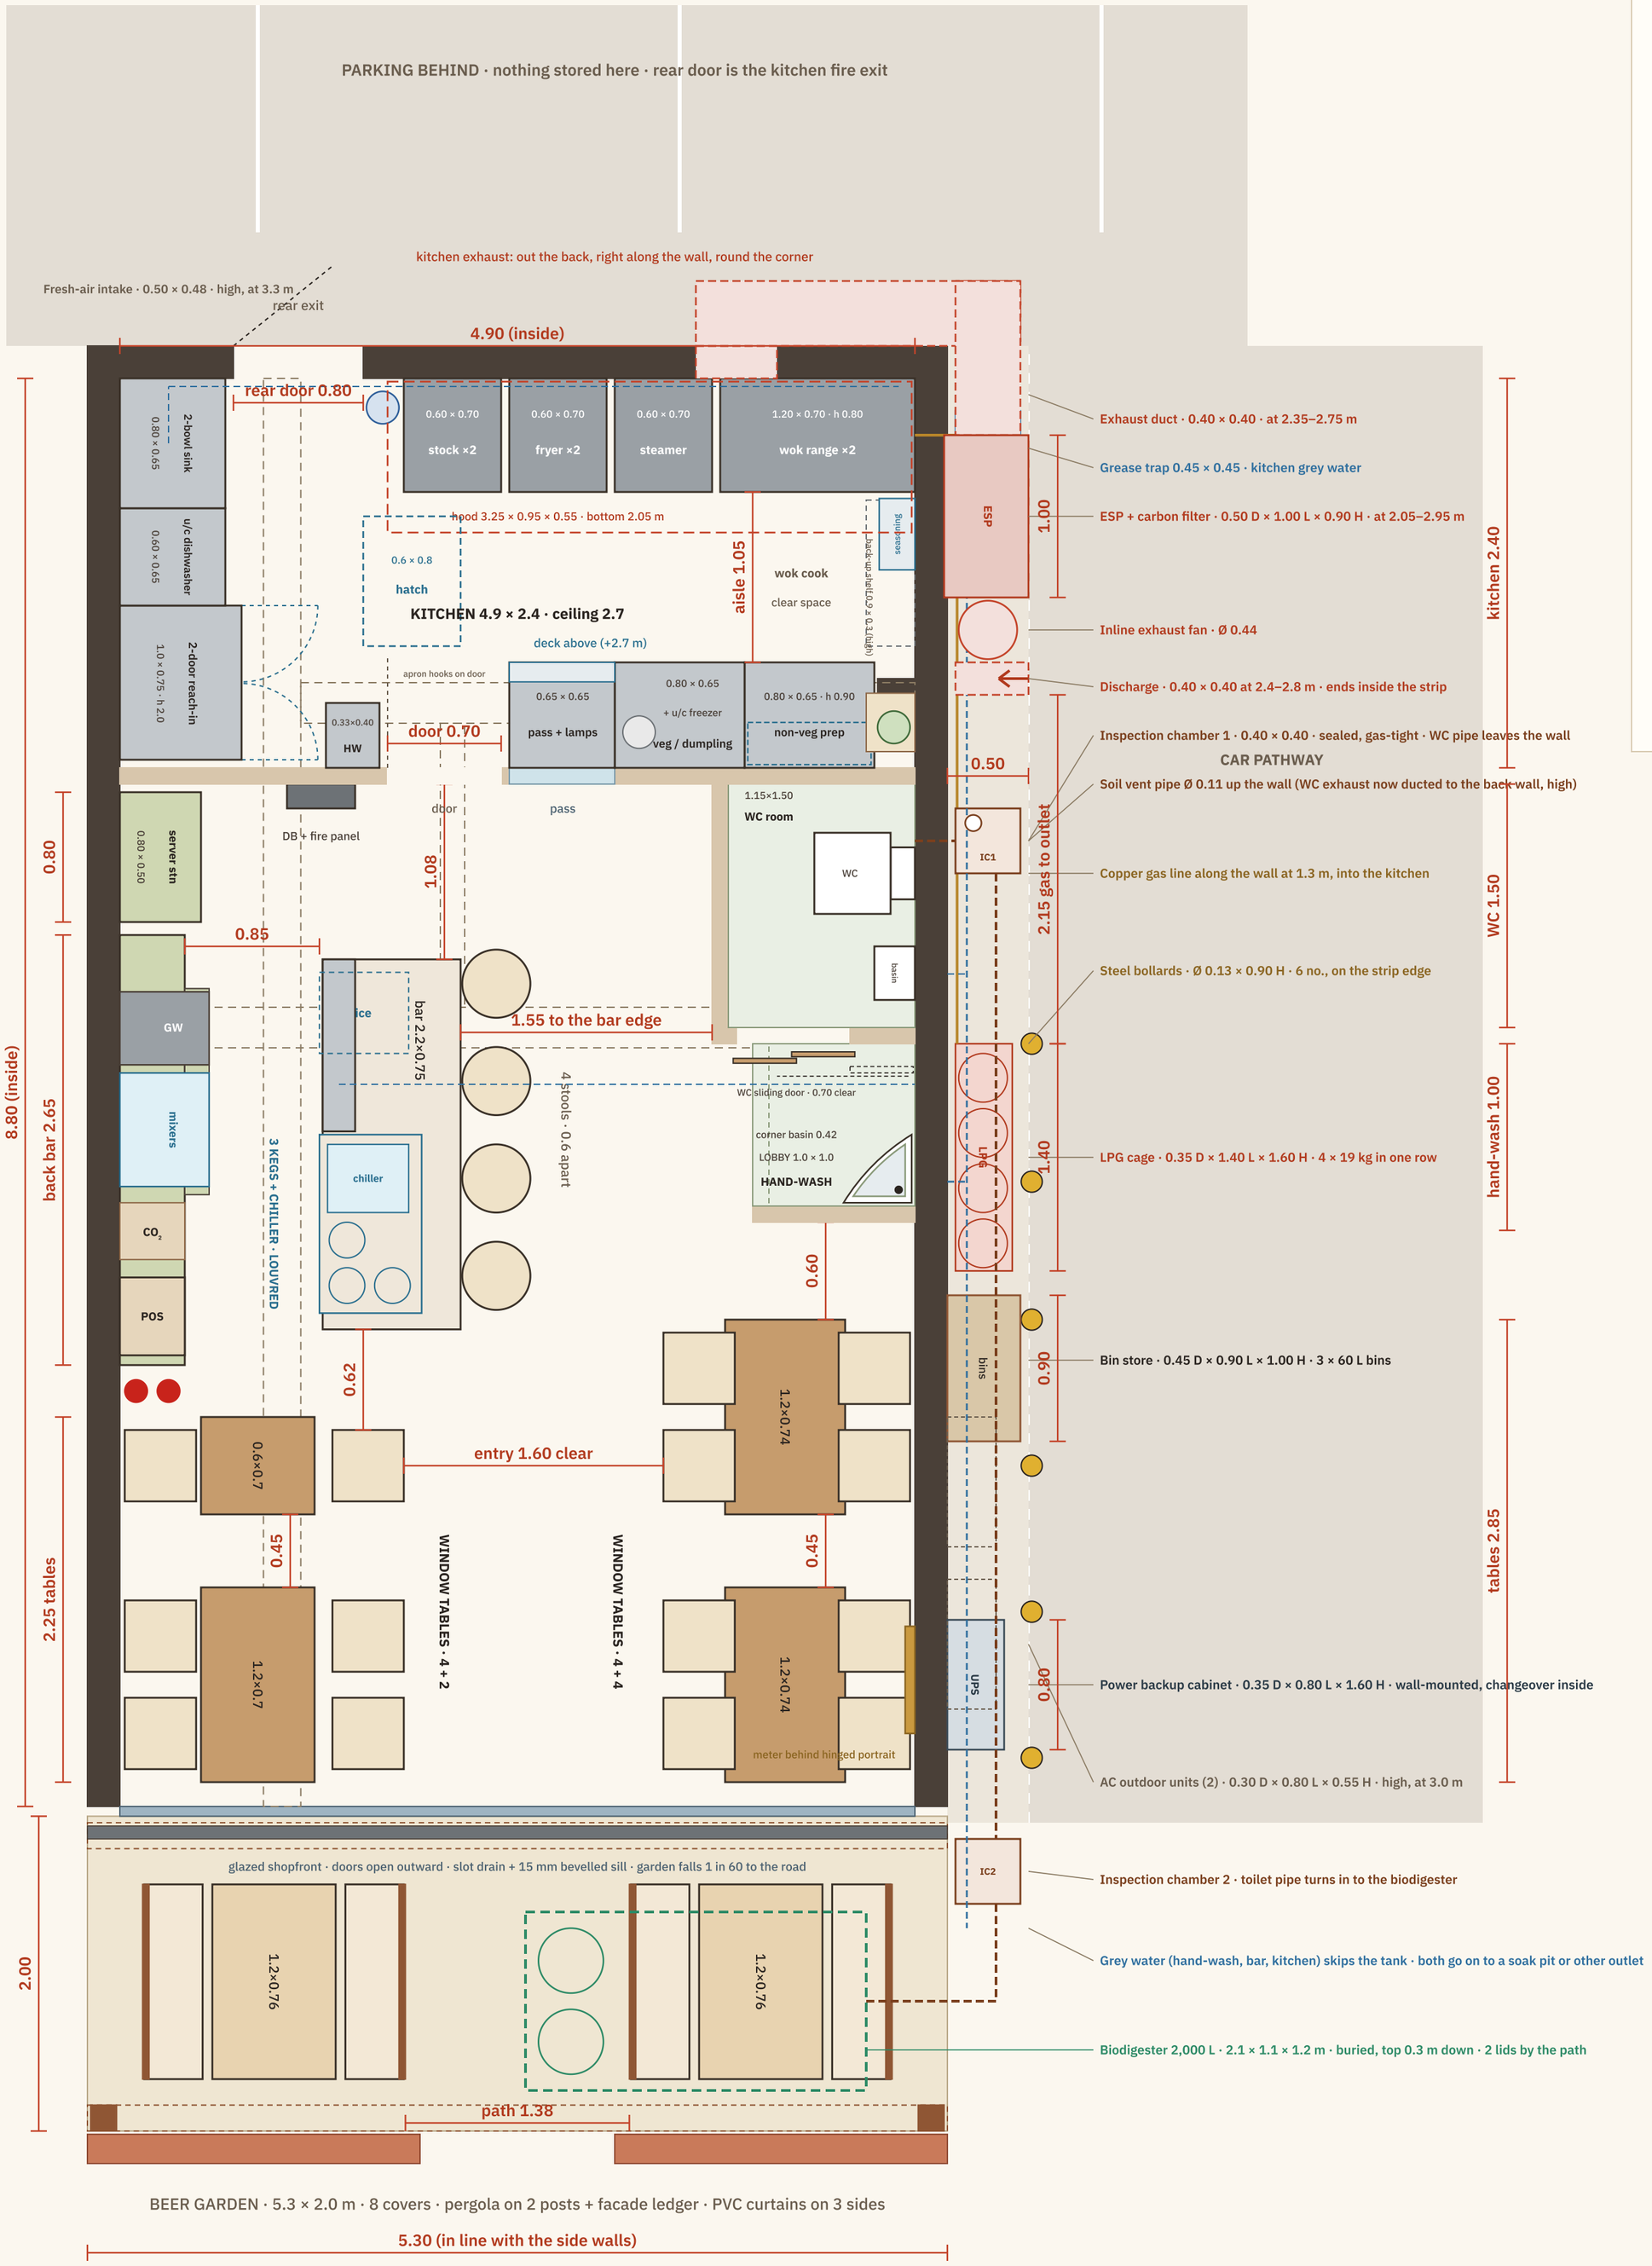

COVERS

Bar stools	4
Window tables, left (4 + 2)	6
Window tables, right (4 + 4)	8
Beer garden, 5.3 × 2.0 m	8
Total	**26**

One double-height room, no loft.
Mirrored: washroom + hand-wash on the right wall drain straight out; bar on the left.
At least 0.45 m between any two tables.
1.6 m entry, 0.62 m window table to bar, 1.1 m at the kitchen door, 1.55 m from the bar edge to the washroom block.
Kitchen sized to the 22-dish menu.
Power backup cabinet (changeover inside); meter stays inside behind a portrait.
Gas, bins, AC, exhaust and drains in a 0.5 m strip on the right, behind bollards; car pathway beyond, parking behind.
WC drains along the strip to a 2,000 L biodigester under the garden (dashed).
Kitchen: seasoning rail by the wok, chilled mise-en-place rail, pass dip + ticket rail, knife strips, board rack, two pedal bins, apron hooks on the kitchen door.
Exhaust and drains shown dashed.

0 1 m 2 m

All dimensions in metres. Left/right as you walk in from the road (road at the bottom). Dashed = overhead beams, hood, hatch and exhaust duct.