
# Ground floor plan · 4.9 × 8.8 m

Cabin East · Concept 27 (mirrored: washroom right, bar left; 0.45 m min between tables) · from the shop drawing (47 m² super built-up) · 18 covers inside + 8 in the garden · 26 in all

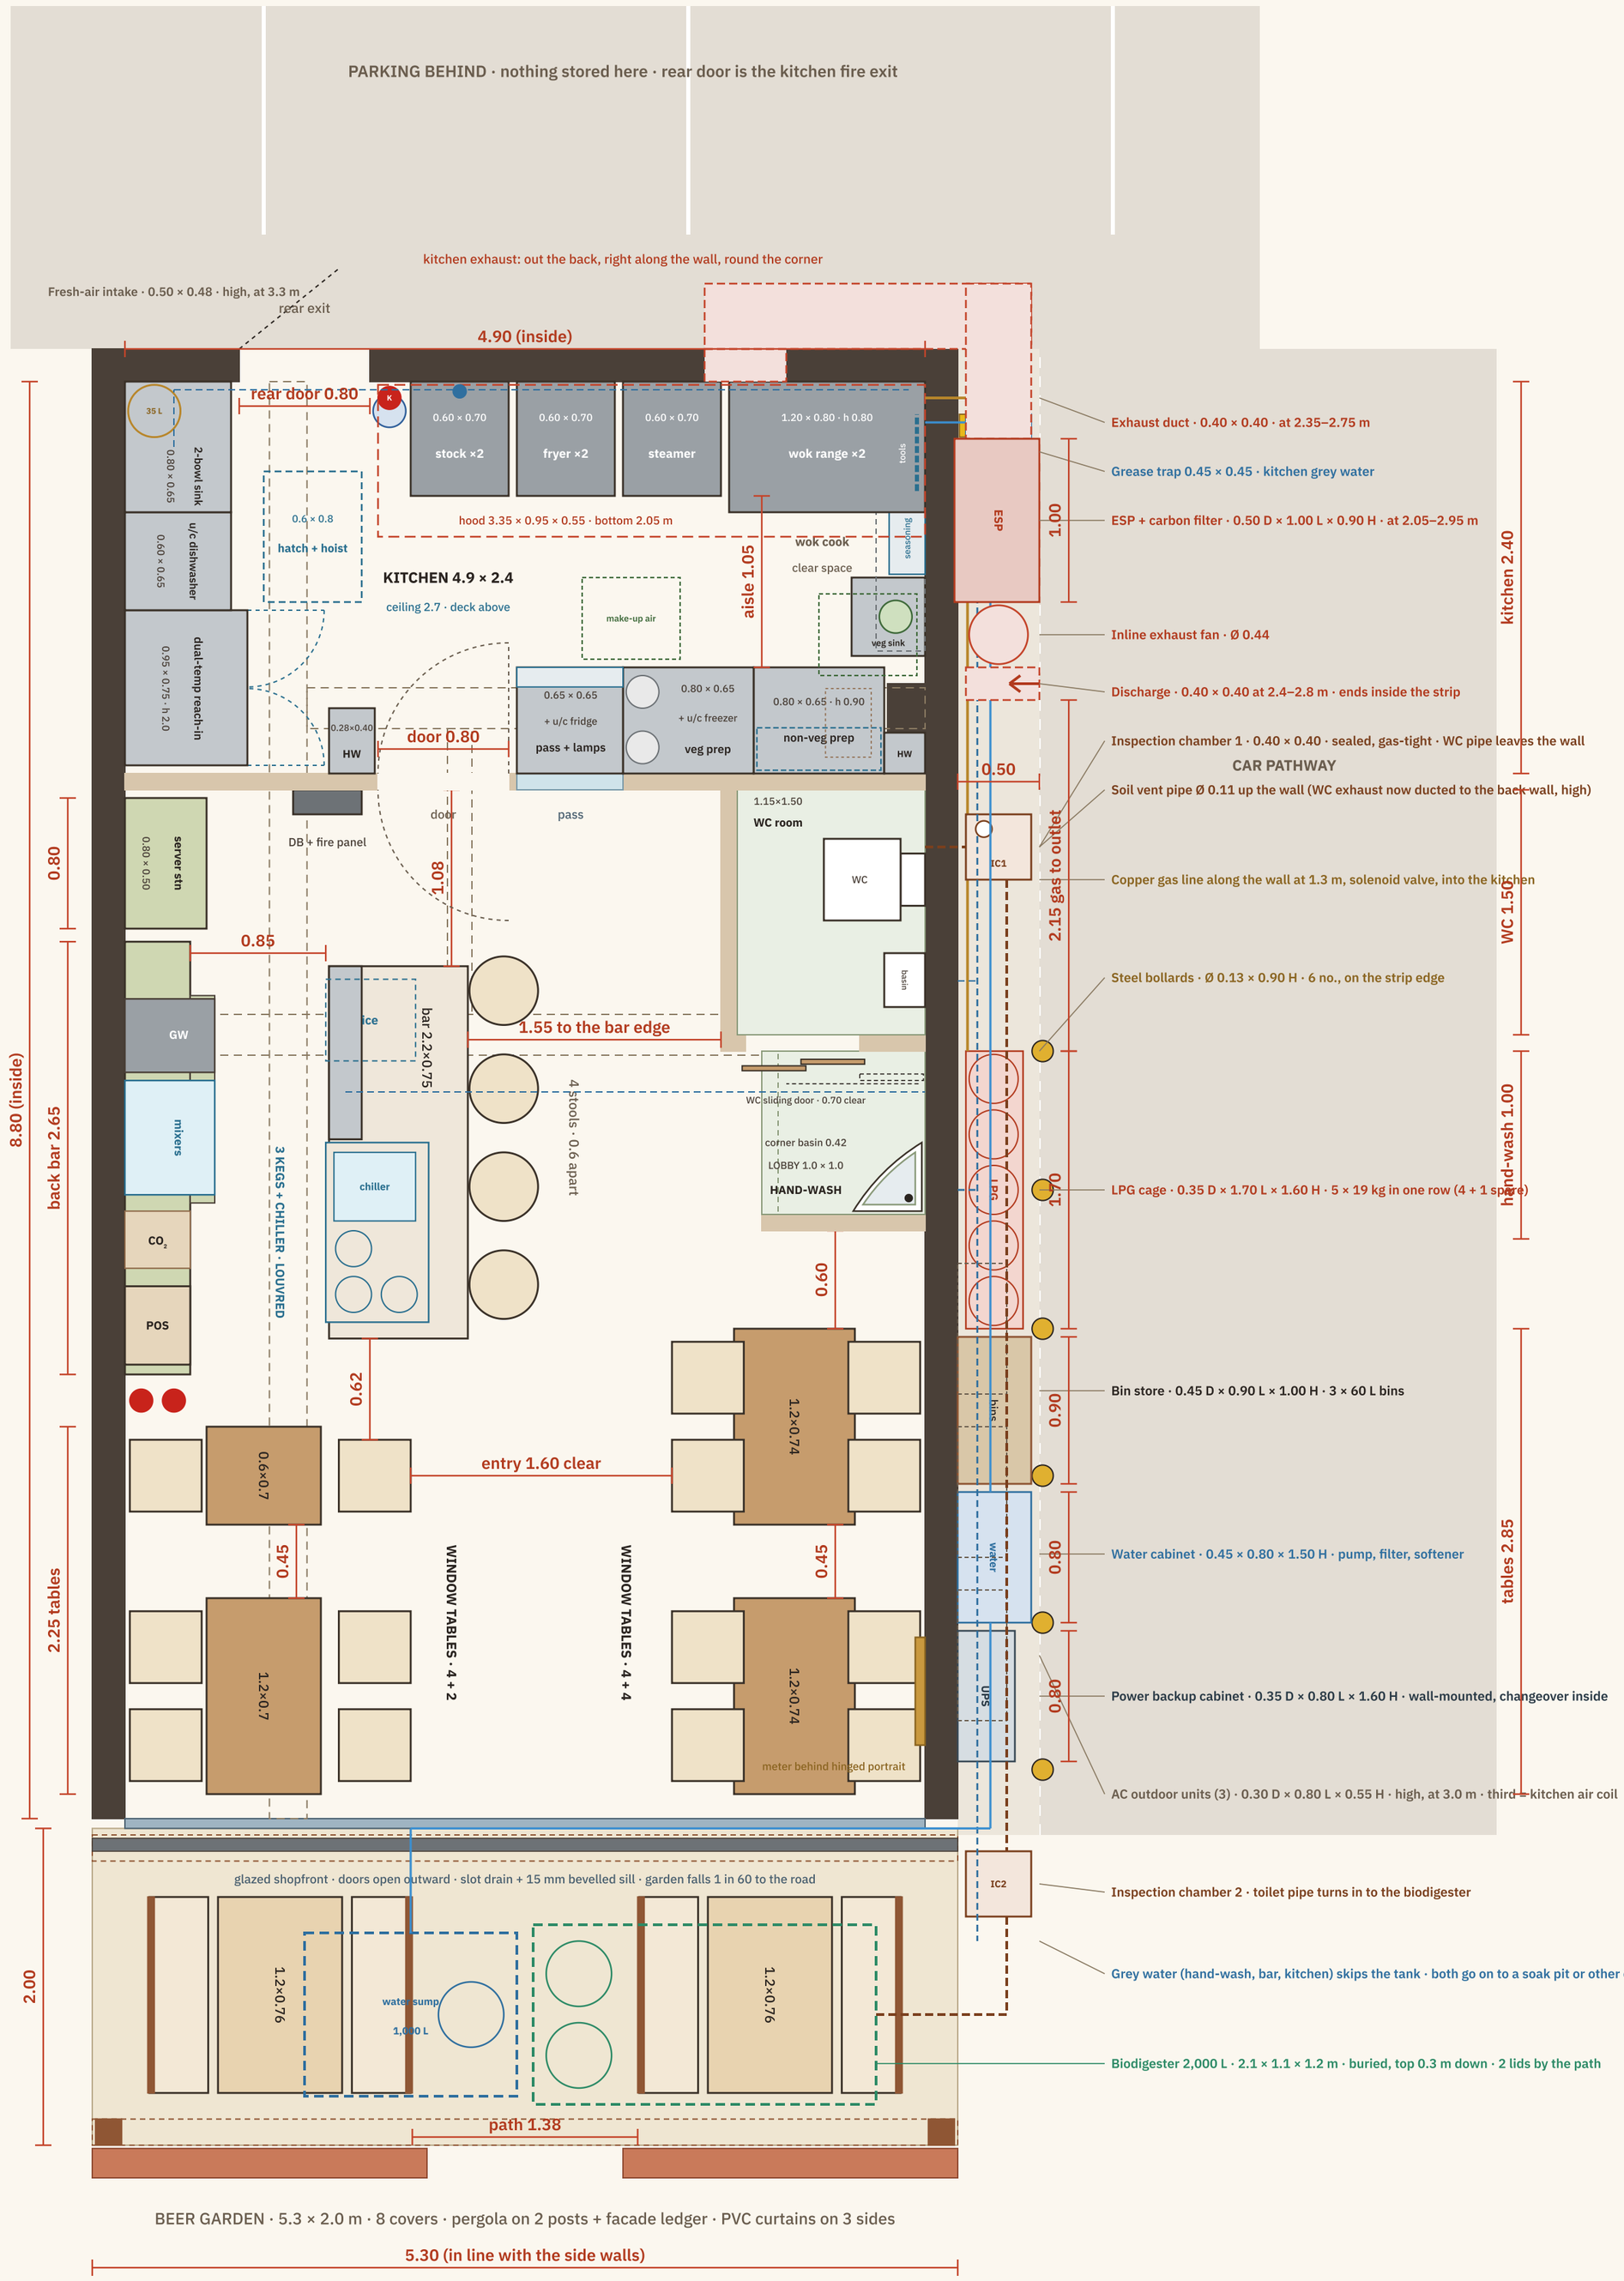


## COVERS

| | |
|---|---|
| Bar stools | 4 |
| Window tables, left (4 + 2) | 6 |
| Window tables, right (4 + 4) | 8 |
| Beer garden, 5.3 × 2.0 m | 8 |
| **Total** | **26** |

One double-height room, no loft.
Mirrored: washroom + hand-wash on the right wall drain straight out; bar on the left.
At least 0.45 m between any two tables.
1.6 m entry, 0.62 m window table to bar, 1.1 m at the kitchen door, 1.55 m from the bar edge to the washroom block.
Kitchen sized to the Pan-Asian menu.
Power backup cabinet (changeover inside); meter stays inside behind a portrait.
Gas, bins, AC, exhaust, water and drains in a 0.5 m strip on the right, behind bollards; car pathway beyond, parking behind.
WC drains along the strip to a 2,000 L biodigester under the garden (dashed).
Kitchen: veg sink and two hand-washes (aprons at the prep corner), 0.8 m double-acting door, dual-temp reach-in, 35 L water heater, pot filler, make-up air, cement-board ceiling, goods hoist at the hatch, seasoning rail, mise-en-place rail, pass fridge, rice cookers, gas solenoid + leak detector, Class K at the end of the hot line.
Water: 1,000 L sump under the left garden → pump, filter, softener on the strip → kitchen.
Exhaust and drains shown dashed.

0 1 m 2 m

All dimensions in metres. Left/right as you walk in from the road (road at the bottom). Dashed = overhead beams, hood, hatch and exhaust duct.