
Kitchen equipment layout

For commercial kitchen equipment vendors · plan at 1:25 on A3 · every item named and sized on the drawing

Cabin East · Wok | Steam | Draught · Concept 27

Sheet 1 of 2 · A3

singhgenics.github.io/Simplex/kitchen.html

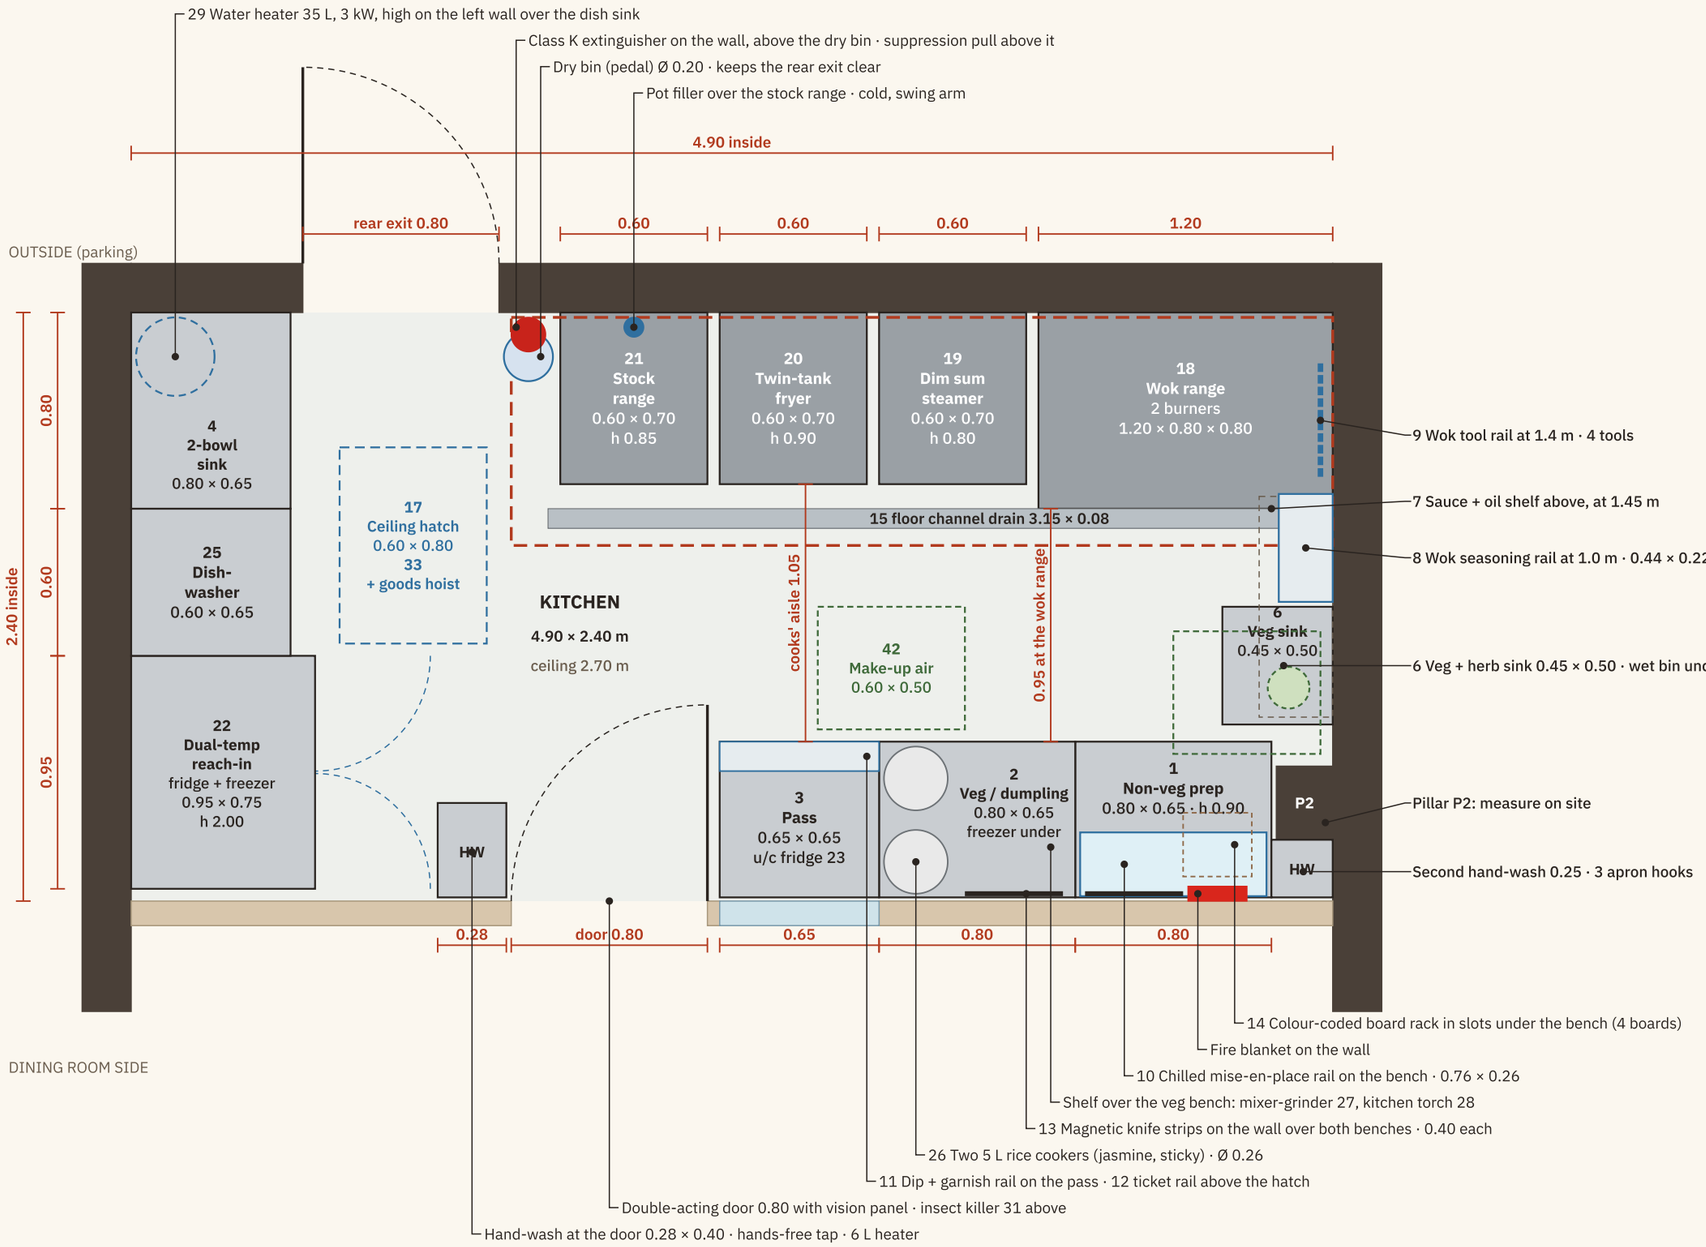

0 — 1 m — 2 m

PLAN 1:25 on A3 · dimensions in metres

Back wall at the top, dining room at the bottom; left and right as you walk in from the road. Dashed red: canopy hood above (3.35 × 0.95, bottom 2.05 m).

Dashed blue: hatch and fridge doors. Dashed green: make-up air diffusers above (2). Dashed grey: shelves above. Heights and services: sheet 2.

Equipment list: the same numbers 1 to 44 as the BOQ

NO	EQUIPMENT / TYPE	SIZE W × D × H (mm)	QTY
	STAINLESS STEEL FABRICATION		
1	Non-veg prep bench	800 × 650 × 900	1 nos
2	Dumpling and veg prep bench	800 × 650 × 900	1 nos
3	Pass counter	650 × 650 × 900	1 nos
4	Dish sink, 2 bowls	800 × 650 × 900	1 nos
5	Wall shelf over the dish line	1,400 × 350	2 nos
6	Veg and herb wash sink	450 × 500 × 900	1 nos
7	Sauce and oil wall shelf	900 × 300	1 nos
8	Wok seasoning rail	440 × 220	1 set
9	Wok tool rail	470 long	1 nos
10	Chilled mise-en-place rail	760 × 260 × 220	1 nos
11	Dip and garnish rail	650 × 120	1 nos
12	Ticket rail	650 long	1 nos
13	Magnetic knife strip	400 long	2 nos
14	Cutting-board rack	280 × 420 × 420	1 nos
15	Floor channel drain	3,150 × 80	3.15 m
16	Storage deck racking	3 sizes, see BOQ	3 nos
17	Ceiling hatch frame with fold-down ladder	600 × 800 opening	1 nos
	COOKING, COLD AND KITCHEN EQUIPMENT (BRANDED)		
18	Chinese wok range, 2 burners	1,200 × 800 × 800	1 nos
19	Dim sum steamer, 2 holes	600 × 700 × 800	1 nos
20	Twin-tank fryer	600 × 700 × 900	1 nos
21	Stock range, 2 burners	600 × 700 × 850	1 nos
22	Reach-in, 2 doors, dual temperature	950 × 750 × 2,000	1 nos
23	Under-counter fridge (pass)	600 × 550 × 700	1 nos
24	Under-counter freezer, 2 doors	fits under 800 × 650	1 nos
25	Under-counter dishwasher	600 × 650 × 900	1 nos
26	Rice cooker	Ø 260	2 nos
27	Mixer-grinder		1 nos
28	Kitchen blowtorch		1 nos
29	Storage water heater	Ø 330 × 500	1 nos
30	Water heater for a hand-wash basin		2 nos
31	Insect killer	500 × 180	1 nos
32	Heat lamp over the pass		2 nos
33	Goods hoist		1 nos
34	Smallware		1 lot
35	Bamboo steamer stack	Ø 260	3 nos
	HOOD, EXHAUST AND VENTILATION		
36	Canopy hood, wall type, with baffle filters	3,350 × 950 × 550	1 nos
37	Exhaust ducting, rectangular	400 × 400	5 m
38	Discharge elbow	400 × 400	1 nos
39	ESP with carbon odour filter	500 × 1,000 × 900	1 nos
40	Inline exhaust fan	Ø 440	1 nos
41	Fresh-air intake fan	500 × 480	1 nos
42	Make-up air diffuser, perforated, low velocity	600 × 500	2 nos
43	Make-up air cooling coil with condenser	condenser 800 × 550 × 300	1 set
44	Exhaust fan and ESP control panel		1 nos
	Gas, plumbing, electrical, civil, fire: main BOQ		

NOTES

Stainless steel 304 benches, 0.90 m high; hot line 0.70 deep, wok range 0.80. Cooks' aisle 1.05 m (0.95 m at the wok range). Cement-board ceiling at 2.70 m; storage deck above, hoist at the hatch. Pan-Asian menu: about 23 recipes, 40 choices; one chef + one helper. The numbers 1 to 44 on the items are the BOQ numbers (boq.html). Positions are from the 3D model: check walls and pillar P2 on site.